




01 / TWO-SPAN BEAM ELEVATION

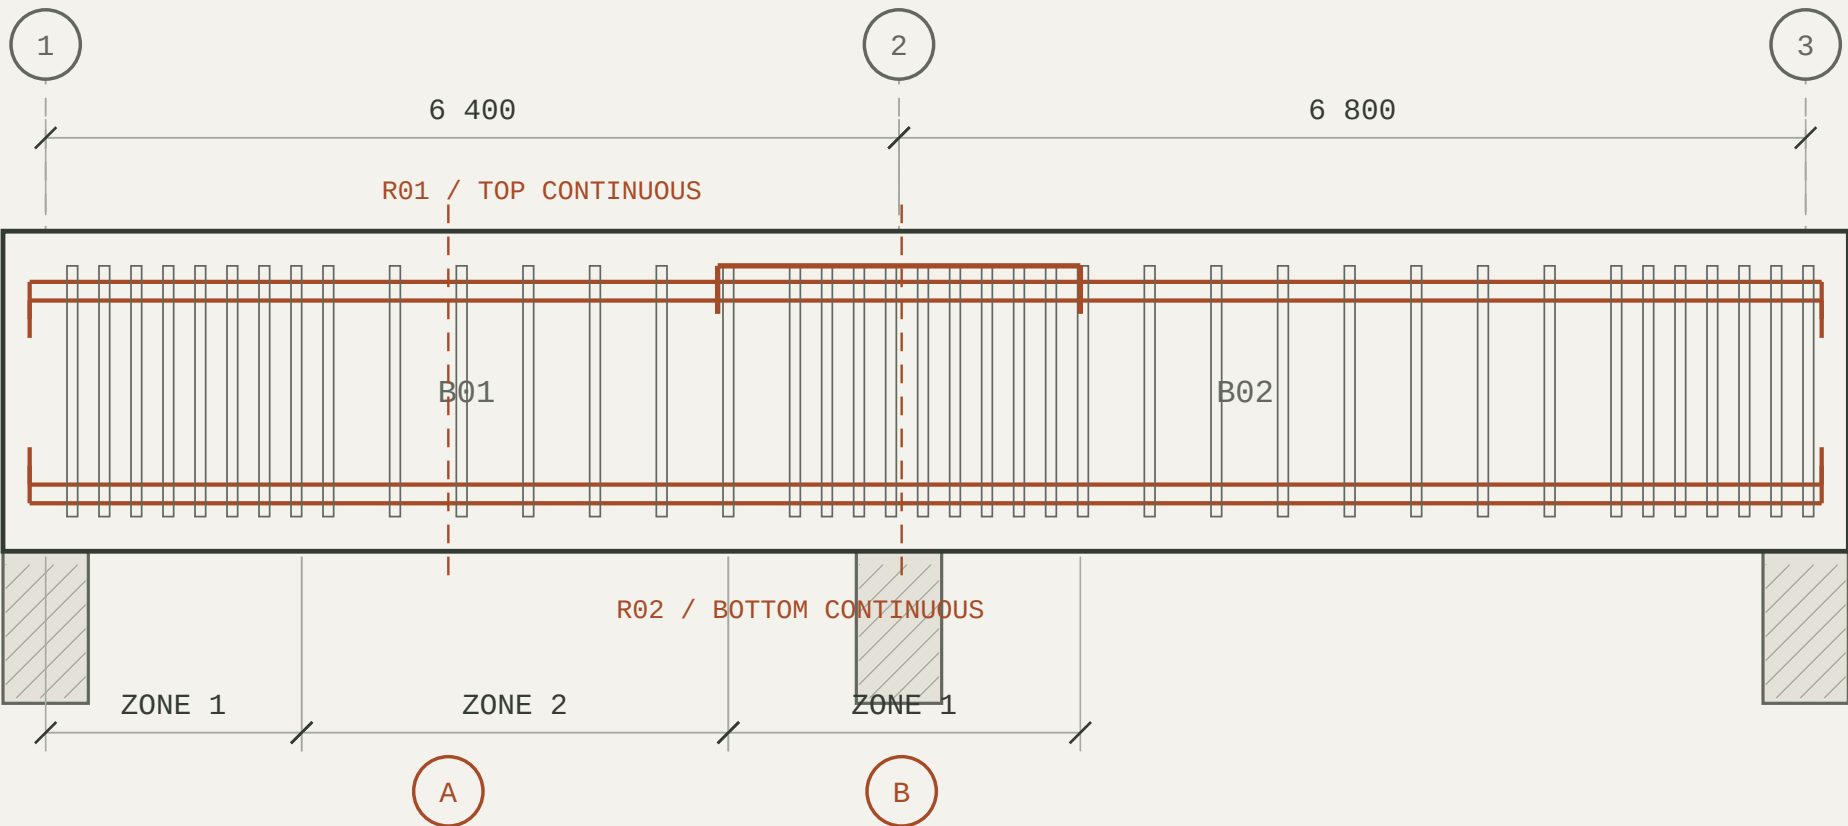


02 / SECTION A-A

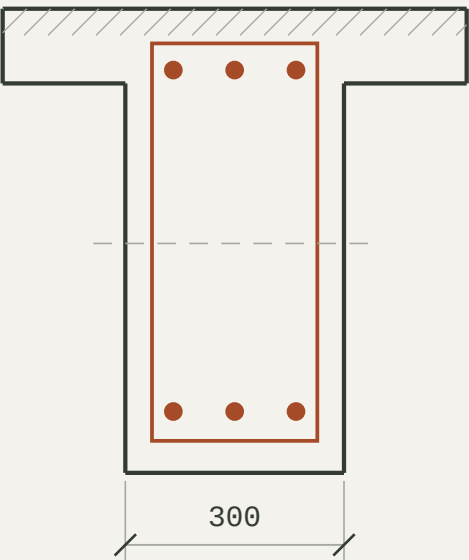

03 / SECTION B-B

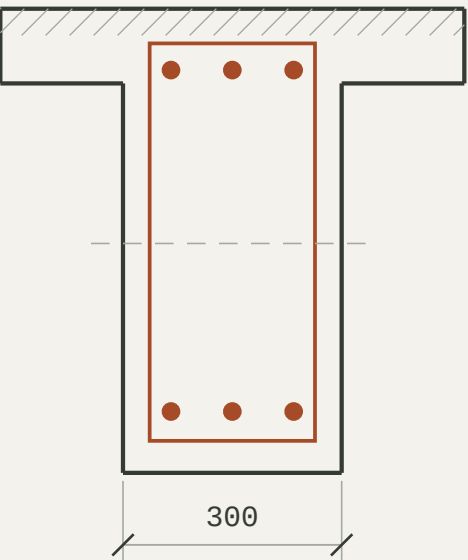

04 / SUPPORT ZONE

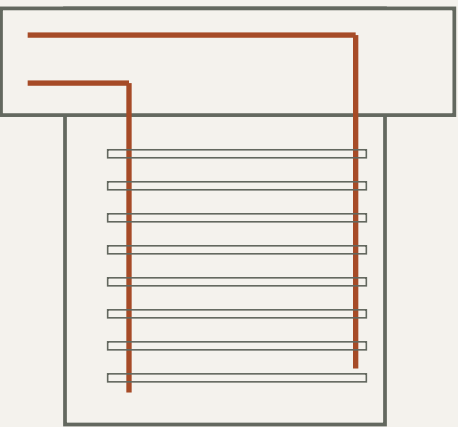

ANCHORAGE STUDY / NTS

REINFORCEMENT REFERENCES

- R01 Continuous top bars
- R02 Continuous bottom bars
- R03 Support-zone bars
- R04 Closed links
- R05 Local anchorage study

BAR ARRANGEMENT / KEY

- Longitudinal reinforcement
- Transverse links
- Concrete outline

RELATED SHEETS

- FW-S01 / Plan and grid location
- FW-S03 / Bar schedule layout
- FW-S05 / Column section study
- Section references belong to this sheet.

DRAWING NOTES

- Bar marks demonstrate drawing hierarchy.
- Reinforcement is not a designed arrangement.
- Anchorage and laps require project design.
- Read sections with the marked elevation.

BEAM REINFORCEMENT STUDY

REINFORCEMENT / SCHEMATIC / NOT TO SCALE

PURPOSE

COMMUNICATION
STUDY ONLY

SHEET / REVISION

FW-S02 / 01