


01 / STRUCTURE + SERVICE INTERFACES

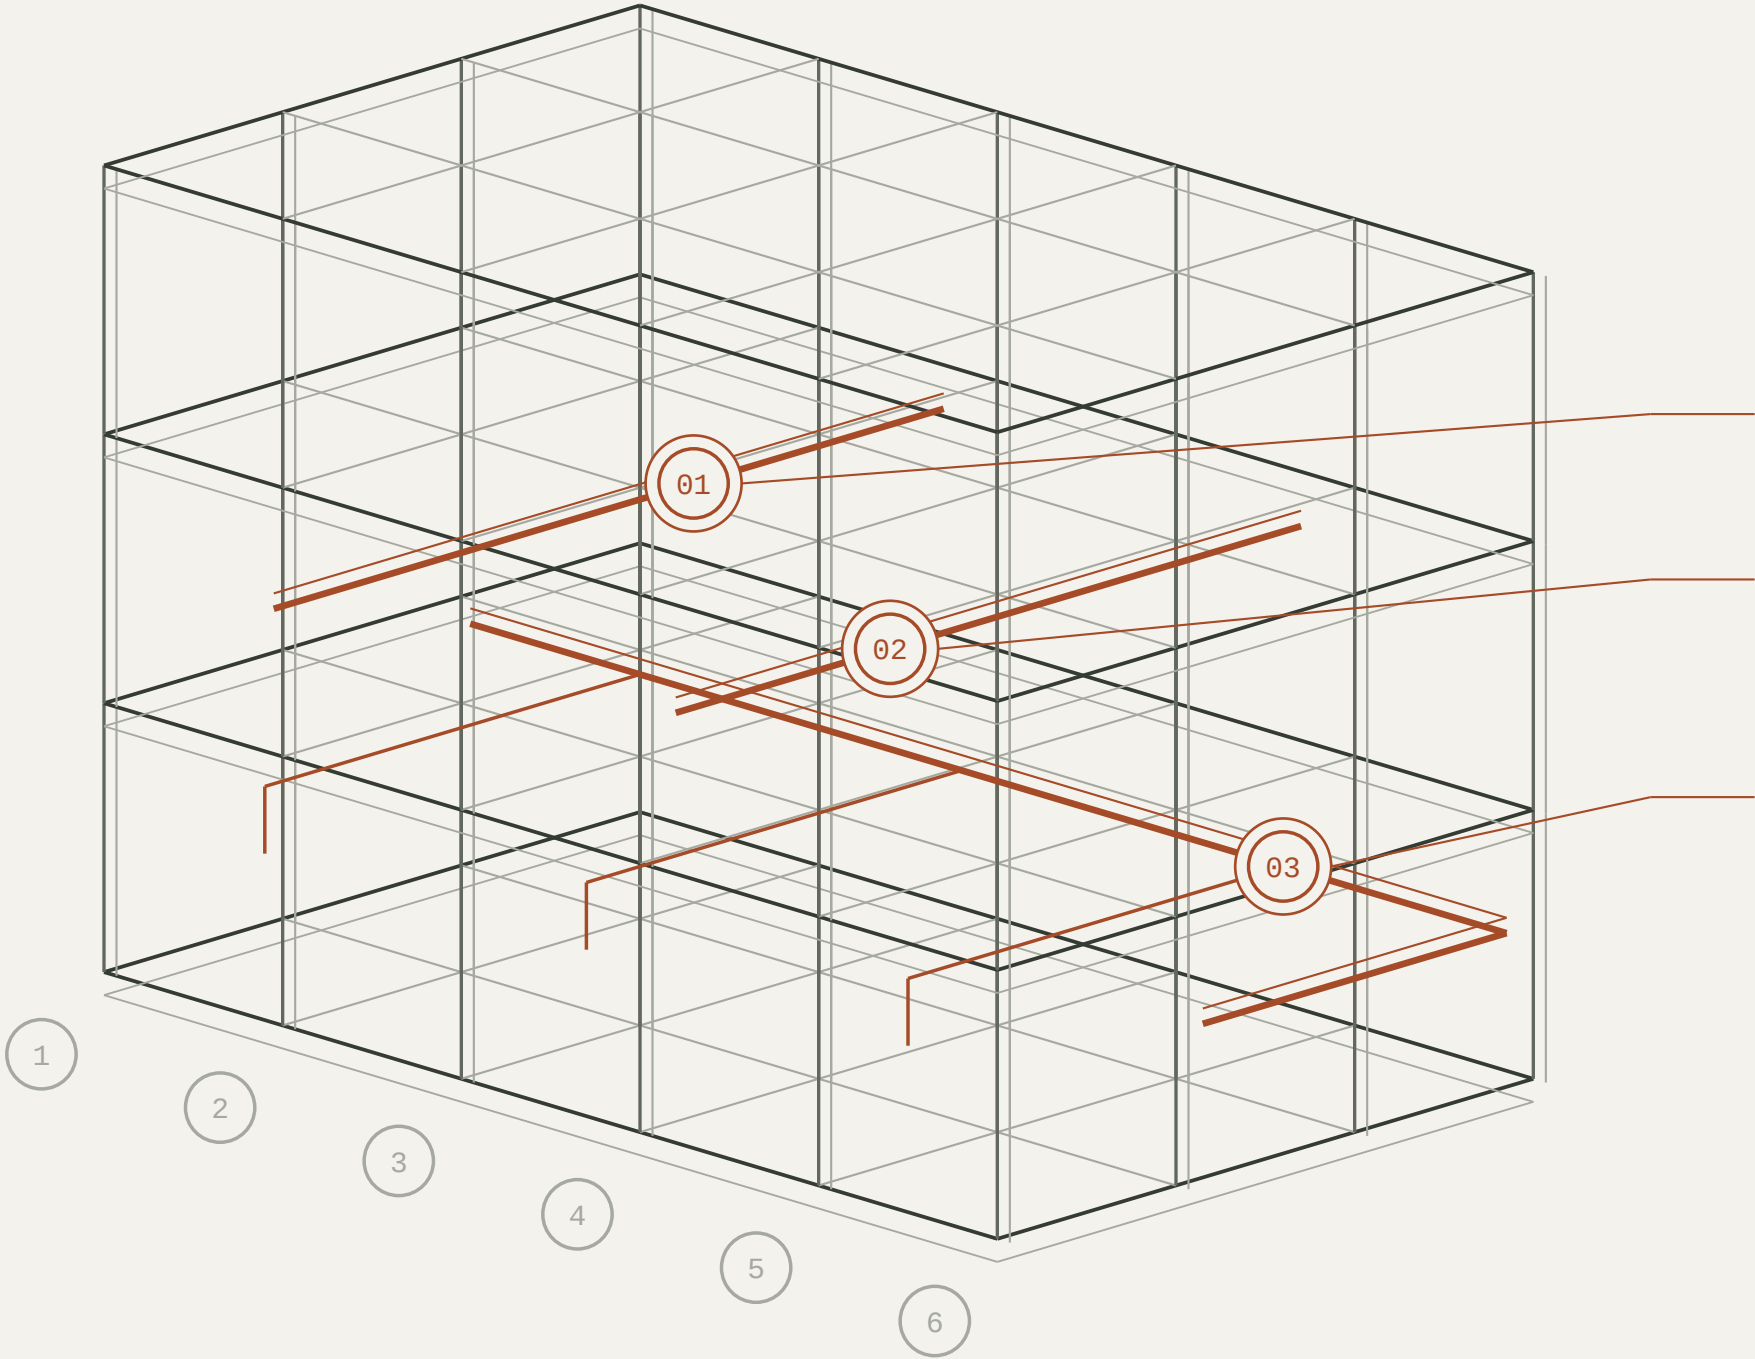

AXONOMETRIC / COORDINATION STUDY / NOT TO SCALE

INTERFACE REVIEW LOG

01 / BEAM CROSSING

Review route against structural depth.


02 / SERVICE RESERVATION

Locate the opening in plan and section.

03 / BRANCH CONNECTION

Review the local installation sequence.

02 / LOCAL INTERFACE SECTION

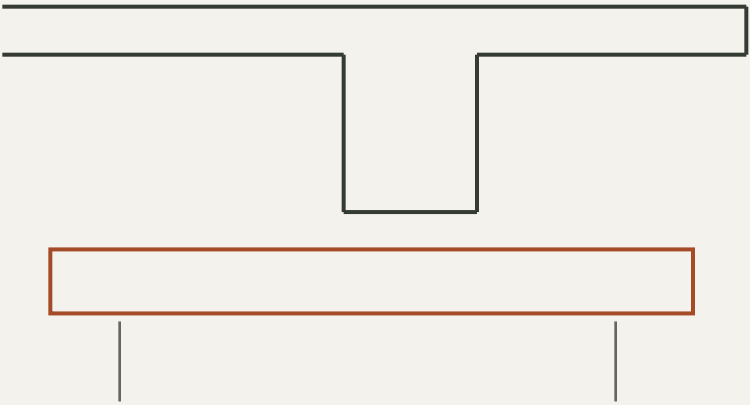

STRUCTURE / RESERVED SERVICE ZONE

DRAWING NOTES

Routes illustrate coordination interfaces.
Highlighted items require project review.
No clearances or openings are approved.
Read the local section with issue 02.

STRUCTURAL INTERFACE VIEW

MODEL VIEWS / SCHEMATIC / NOT TO SCALE

PURPOSE

COMMUNICATION
STUDY ONLY

SHEET / REVISION

FW-S04 / 01