



01 / STRUCTURAL FLOOR PLAN

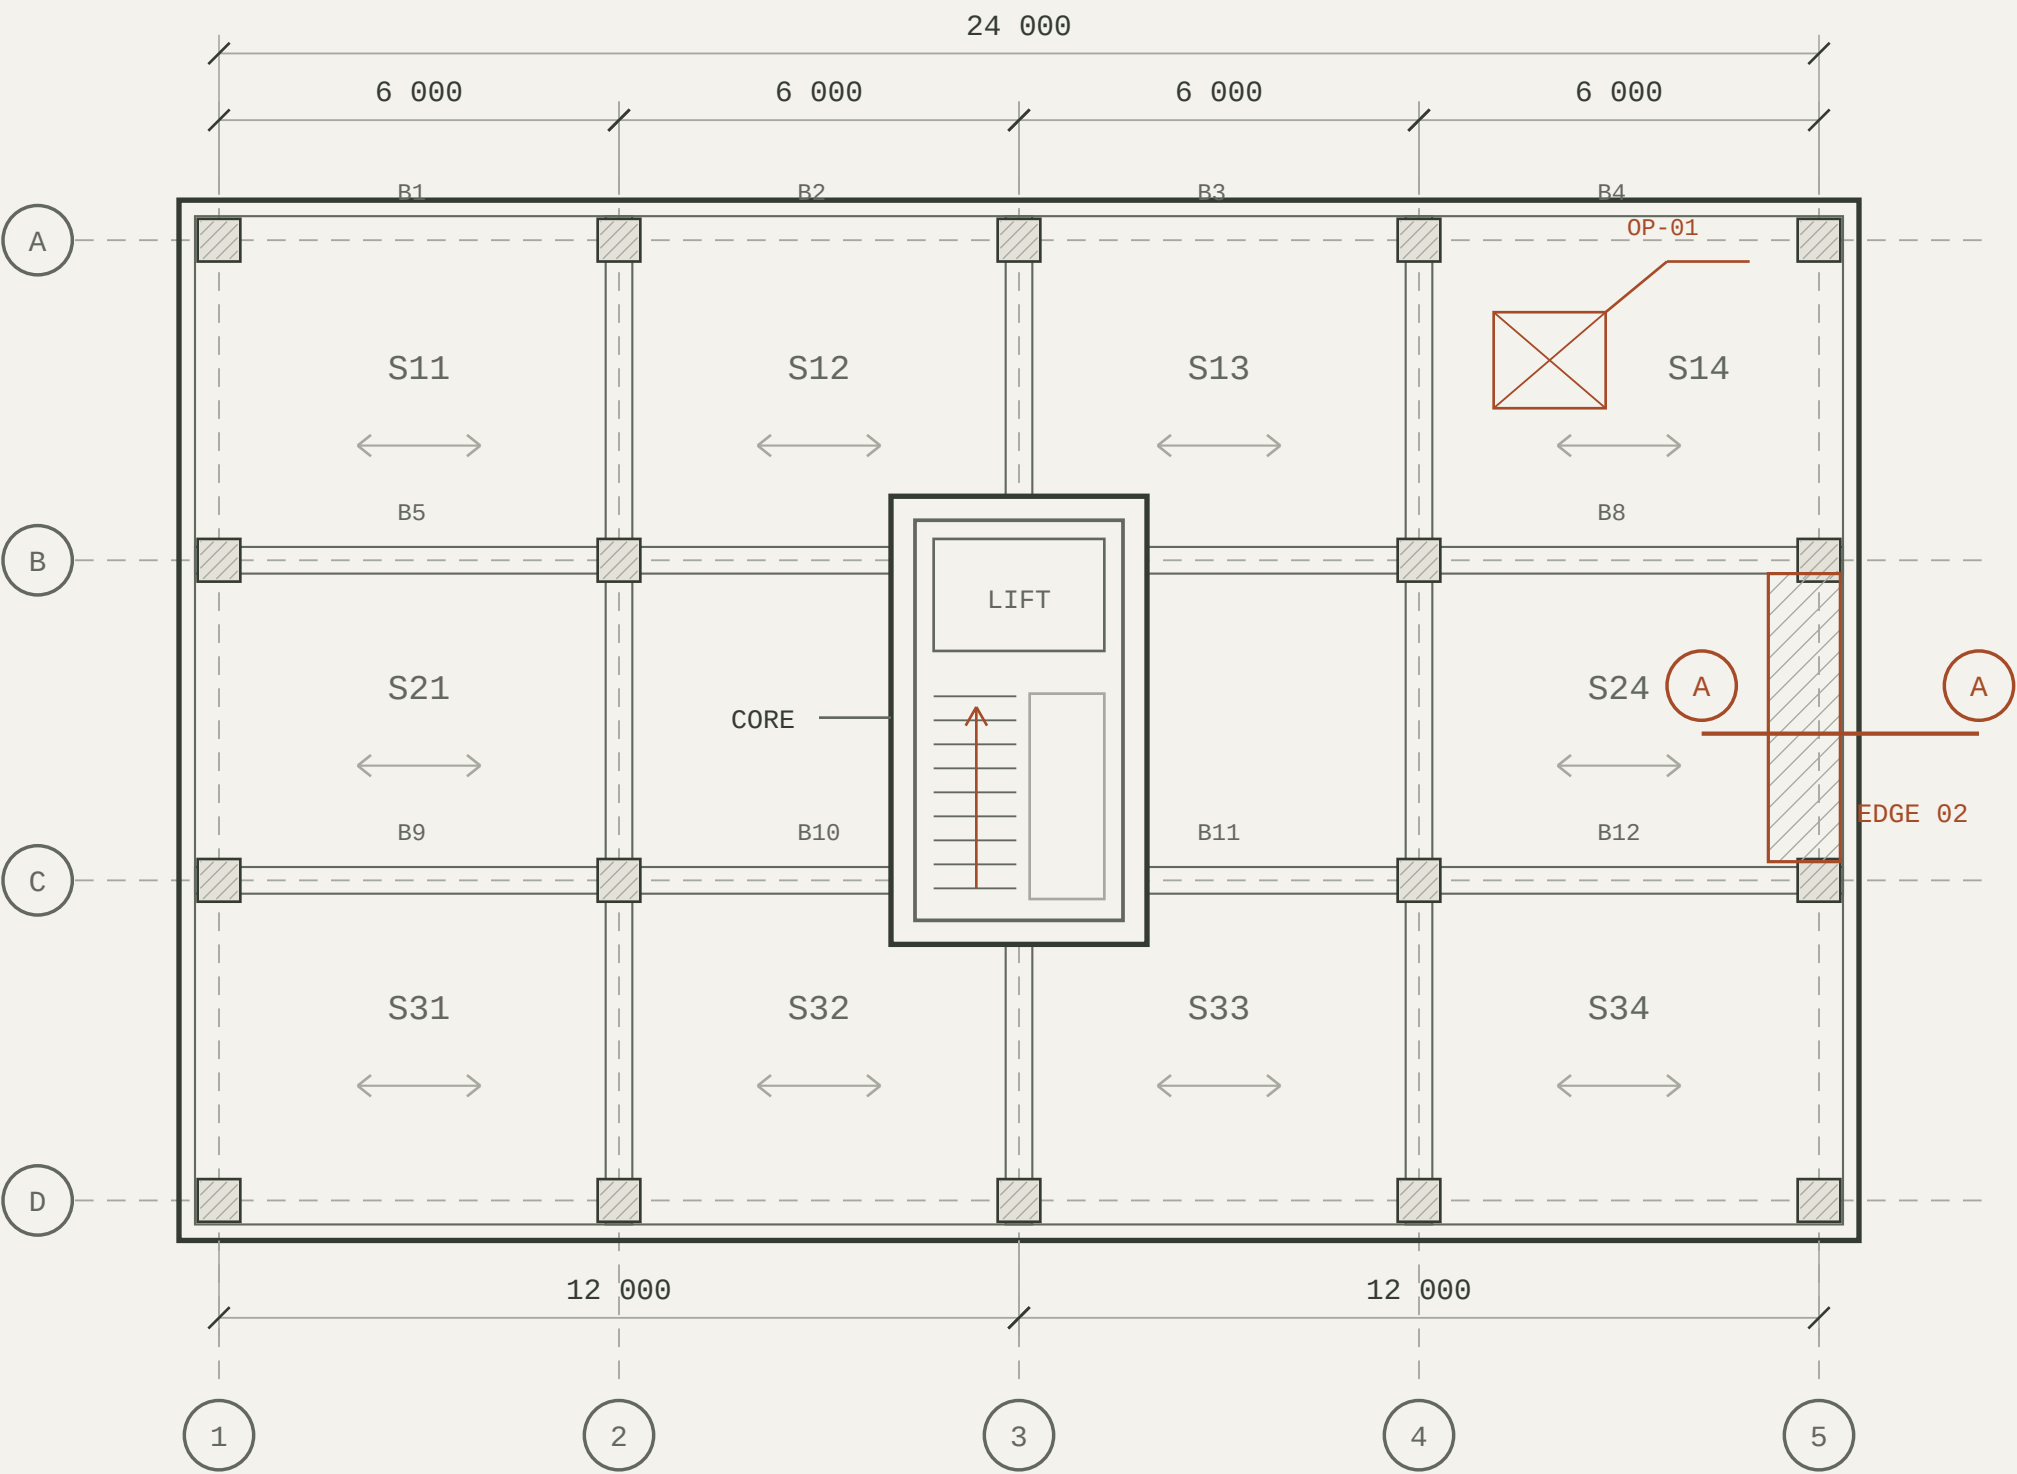

ALL DIMENSIONS IN mm / ILLUSTRATIVE VALUES ONLY

KEY PLAN / SECTION LOCATION

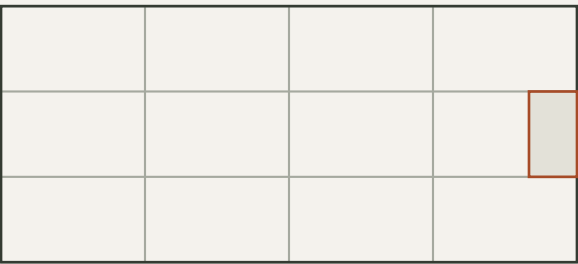


A-A / EAST EDGE -> DETAIL 02

DRAWING KEY

- Sxx Slab zone reference
- Bxx Beam reference
- OP-01 Service opening study
- A-A Section location

02 / EDGE SECTION A-A

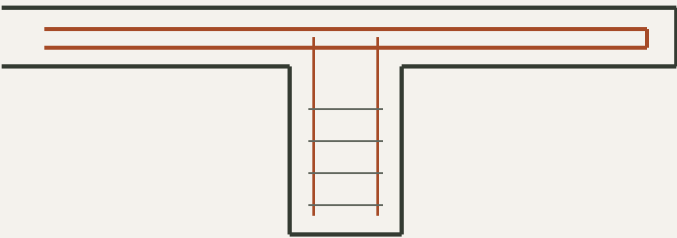

SLAB / SUPPORT RELATIONSHIP

DRAWING NOTES

- Grid dimensions are illustrative only.
- Coordinate openings with service routes.
- Read the edge section with its plan marker.
- Geometry is not a structural design.

TYPICAL SLAB ARRANGEMENT

SHOP DRAWINGS / SCHEMATIC / NOT TO SCALE

PURPOSE

COMMUNICATION
STUDY ONLY

SHEET / REVISION

FW-S01 / 01